
ს.ს. თიბისი ბანკის
ახალი სერვის ცენტრი
ქ. თბილისი, აბაშიძის და
არაყიშვილის კუთხეში

კონსტრუქციული ნაწილი

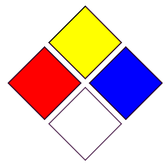

შ.პ.ს. „სუჯა“

თბილისი 2017 წ.

განმარტებითი ბარათი

წინამდებარე რეკონსტრუქციის პროექტის კონსტრუქციული ნაწილი შედგენილია შპს „სუჯა“-სა და „სს თიბისი ბანკს“ შორის დადებულ ხელშეკრულების საფუძველზე და არქიტექტურული ნაწილის მიხედვით.

პროექტის შედგენისას (კონსტრუქციული ნაწილი) გამოყენებულია დღეისათვის საქართველოში მოქმედი სამშენებლო ნორმები და წესები (ყოფილი მშენებლობის სამინისტროს ბრძანება №3/26, 05. 2002 წ. და 2006 წ. 24. 02 დადგენილება №45). კერძოდ: 1). სნ-წ-2.01.07.-85 „დატვირთვები და ზემოქმედებანი“; 2). სნ-წ-II-7-81 „მშენებლობა სეისმურ რაიონებში“; 3). სნ-წ-2.03.01.-84 „ბეტონისა და რკინაბეტონის კონსტრუქციები“; 4) პნ 03.01-09, „ბეტონისა და რკინაბეტონის კონსტრუქციები“; 5) პნ 01.05-08, „სამშენებლო კლიმატოლოგია“; 6) პნ 01.01-09, „სეისმომედეგი მშენებლობა“ .

საპროექტო დავალება მიიძნად ისახავს არსებული რკინაბეტონის პანდუსის დემონტაჟს რომელზეც ხდებოდა კიბის მოწყობა, ხოლო დარჩენილი ღიობი იხურება რკინაბეტონის ფილით, ასევე შესავსებია ანტრესოლის სართულზე (+3,31 ნიშნულზე) „1“ და „ა“ „ბ“ ღერძებში მდებარე არსებული ღიობი, რომელიც ივსება ასევე რკინაბეტონის ფილით.


ნახაზების ჩამონათვალი

№	ნახაზის დასახელება	ნახაზის ნომერი
1	ნახაზების ჩამონათვალი, სპეციფიკაცია, განმარტებითი ბარათი	კ-1
2	გეგმა 0,00 ნიშნულზე	კ-2
4	გეგმა +3,31 ნიშნულზე	კ-3
5	კვეთები; 1-1; 2-2; 3-3	კ-4

მასალათა სპეციფიკაცია

ელემენტი	პოზ.№	ესკიზი მმ.	დიამეტრი და კლასი	L მმ.	n ცალი	nxL მ.	არმატურის ამოკრეფა			
							დიამეტრი და კლასი	ΣnxL მ.	მასა კგ.	
									A-I	A-III
1	2	3	4	5	6	7	8	9	10	11
რ/ბ-ის ფილები +0.00 და +3.31 ნიშნულებზე	1	დაიჭრას ადგილზე	12A-III			840	6A-I	44,8	9,9	
	2	40 200 40	6A-I	280	160	44,8	12A-III	840,0		745,92
							ჯამი		9,9	745,9
							ბეტონის კლასი სიმტკიცის მიხედვით B25 V=5.0 მ3.			

ფორ. A-3	დაკვეთა		
ექსპლიკაცია			
პირობითი ნიშნები			
შენიშვნები:			
დამკვეთი	ს.ს. თიბისი ბანკი		
მისამართი	მარჯანიშვილის გამზირი №7		
პროექტის სახელწოდება	ს.ს. თიბისი ბანკის ახალი სერვის ცენტრი ქ. თბილისი, აბაშიძის და არაყიშვილის კუთხე		
თანამდებობა	გვარი	ხელმოწერა	
დირექტორი	ზ. სუჯაშვილი		
არქიტექტორი	ბ. სუჯაშვილი		
კონსტრუქტორი	ლ.კვირიკაშვილი		
შ.პ.ს. „სუჯა“			
კონსტრუქციული ნაწილი			
მასშტაბი	1 : 100	განმარტებითი ბარათი მასალათა სპეციფიკაცია ნახაზების ჩამონათვალი	
თარიღი	2017 წ.		
სტადია	ფურცელი	ფურცლები	
კ	კ-04	1	

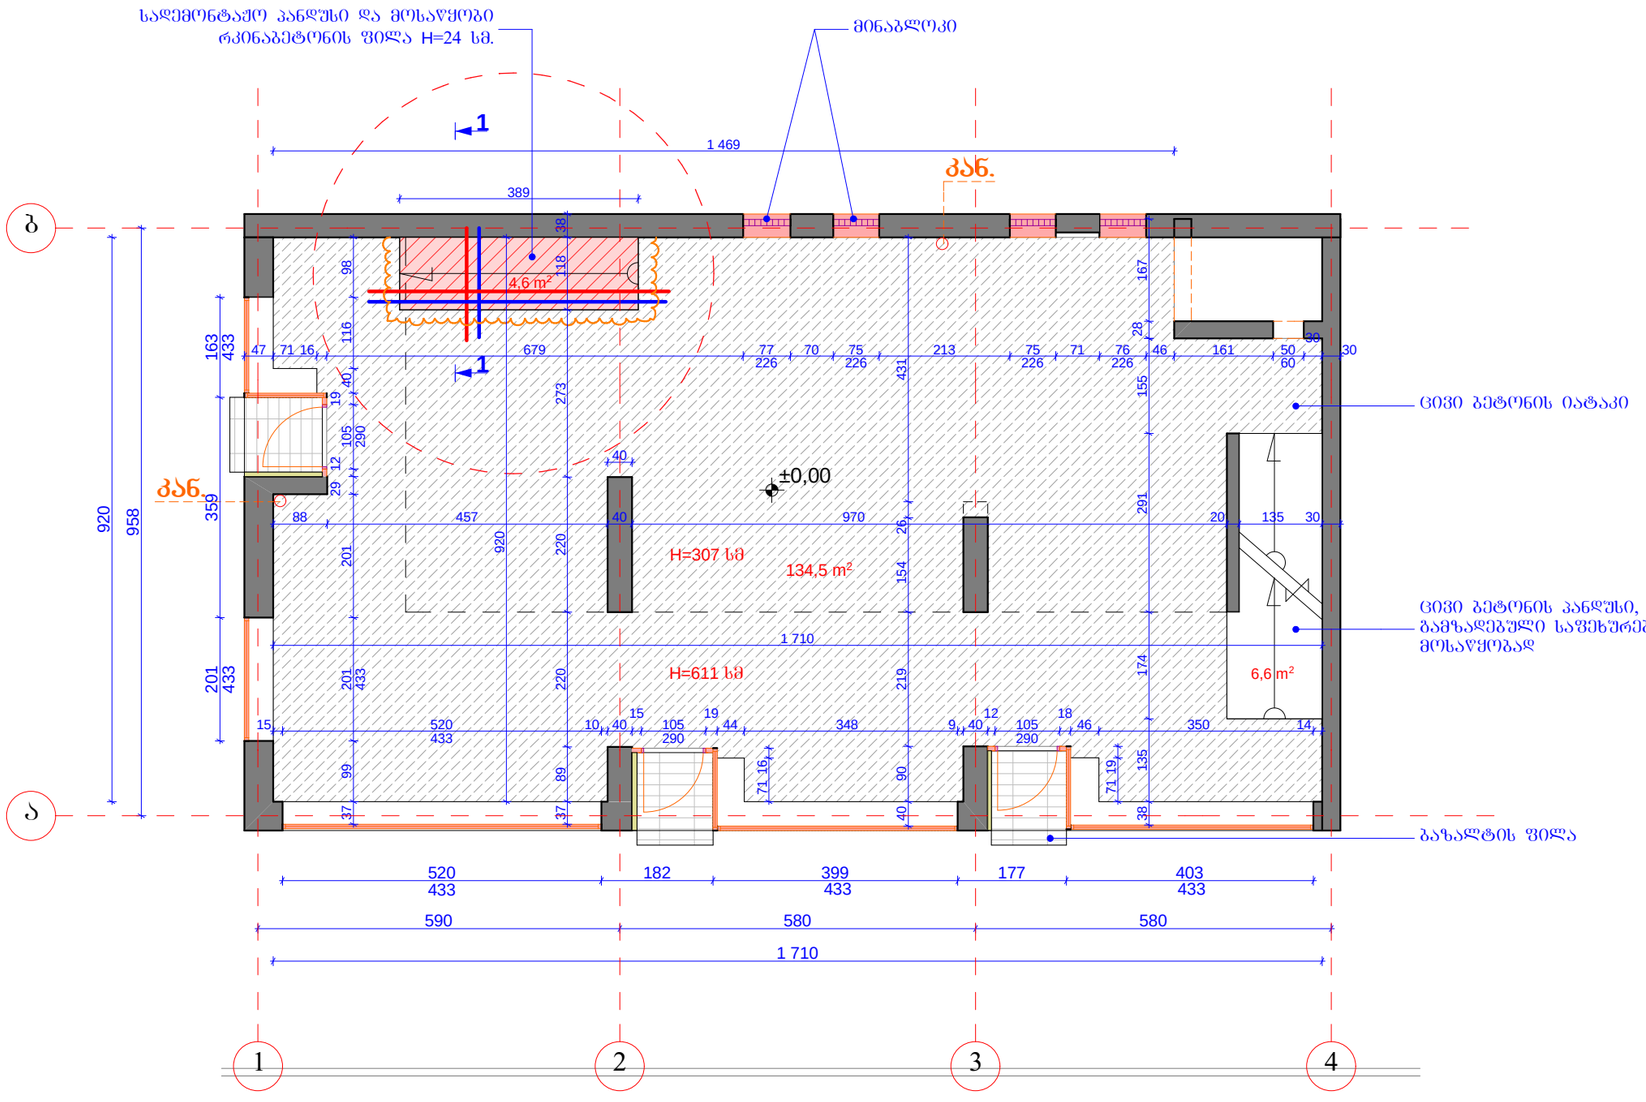

ფორ. A-3	დაკვეთა

ექსპლიკაცია

პირობითი ნიშნები

±0.00 არქიტექტურული ნიშნული

1 – ჭრილის ხაზი

კედელი

შენიშვნები:

დამკვეთი	ს.ს. თიბისი ბანკი
მისამართი	მარჯანიშვილის გამზირი №7
პროექტის სახელწოდება	ს.ს. თიბისი ბანკის ახალი სერვის ცენტრი ქ. თბილისი, აბაშიძის და არაყიშვილის კუთხე

თანამდებობა	გვარი	ხელმოწერა
დირექტორი	ზ. სუჯაშვილი	
არქიტექტორი	ბ. სუჯაშვილი	
კონსტრუქტორი	ლ.კვირიკაშვილი	


შ.პ.ს. „სუჯა“

კონსტრუქციული ნაწილი

მასშტაბი	1 : 100
თარიღი	20176 წ.

გეგმა 0.00 ნიშნულზე

სტადია	ფურცელი	ფურცლები
კ	კ-02	4

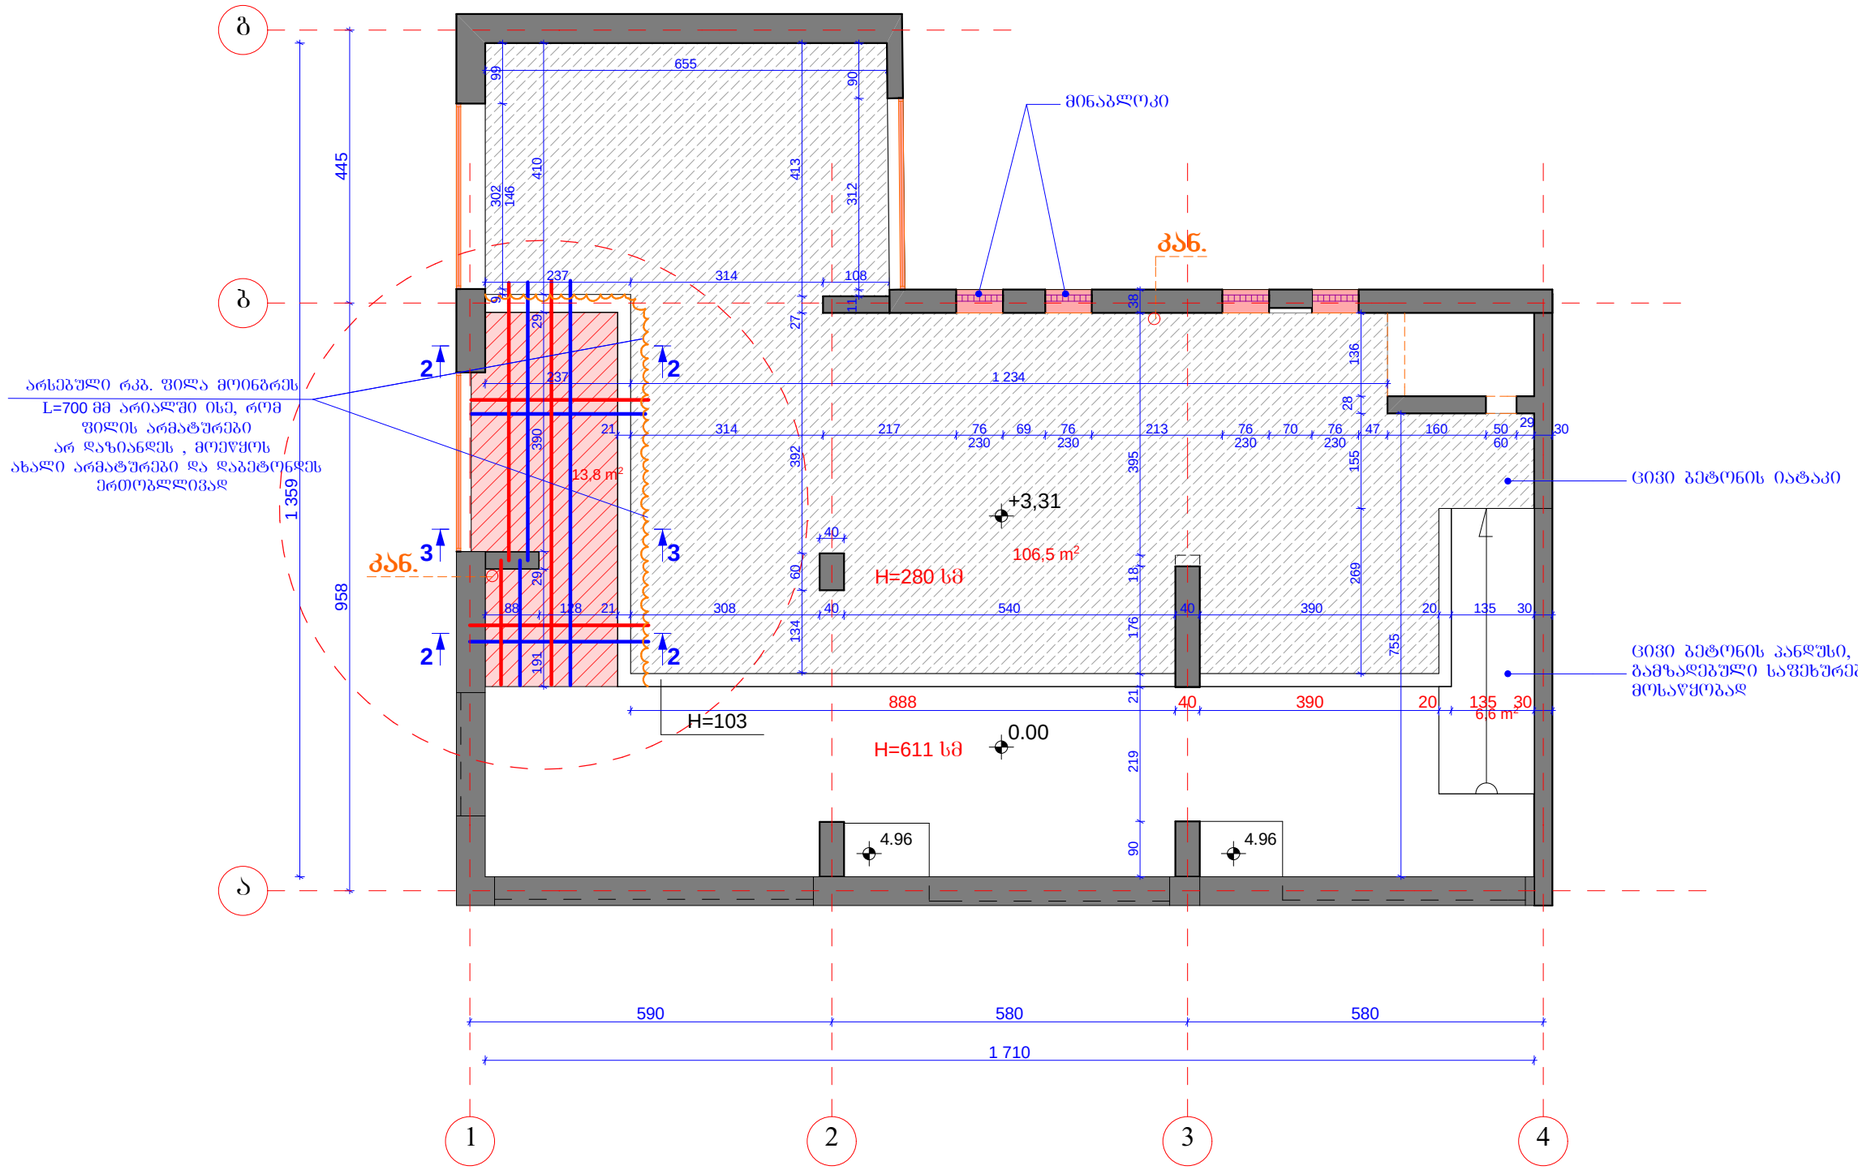

ფორ. A-3 | დაკვეთა

ექსპლიკაცია

პირობითი ნიშნები

+3.31 არქიტექტურული ნიშნული

1 – ჭრილის ხაზი

კედელი

შენიშვნები:

დამკვეთი	ს.ს. თიბისი ბანკი
მისამართი	მარჯანიშვილის გამზირი №7
პროექტის სახელწოდება	ს.ს. თიბისი ბანკის ახალი სერვის ცენტრი ქ. თბილისი, აბაშიძის და არაქიშვილის კუთხე

თანამდებობა	გვარი	ხელმოწერა
დირექტორი	ზ. სუჯაშვილი	
არქიტექტორი	ბ. სუჯაშვილი	
კონსტრუქტორი	ლ.კვირიკაშვილი	

შ.პ.ს. „სუჯა“


კონსტრუქციული ნაწილი

მასშტაბი	1 : 100
თარიღი	2017 წ.


გეგმა +3.31 ნიშნულზე

სტადია	ფურცელი	ფურცლები
კ	კ-03	4


კვეთი 1-1

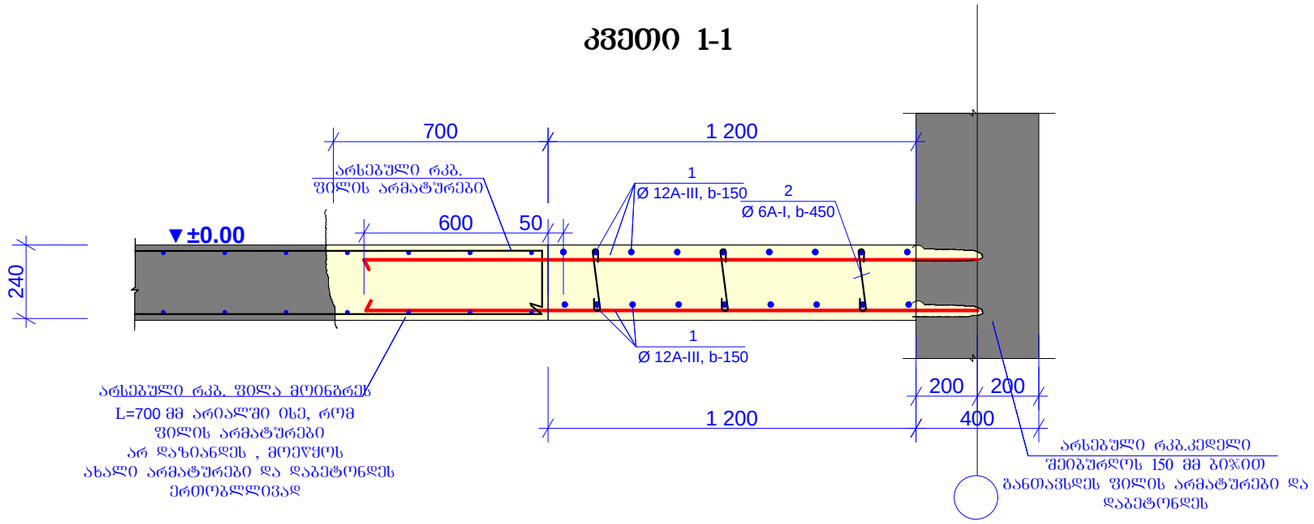

კვეთი 2-2

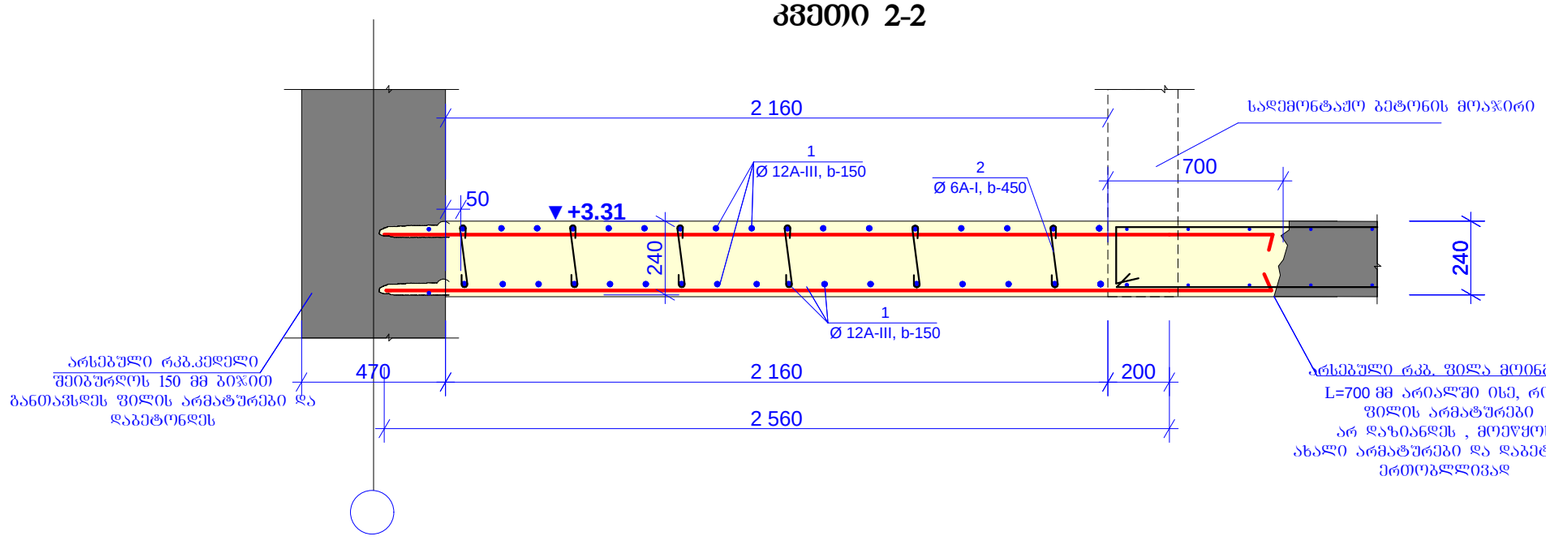

კვეთი 3-3

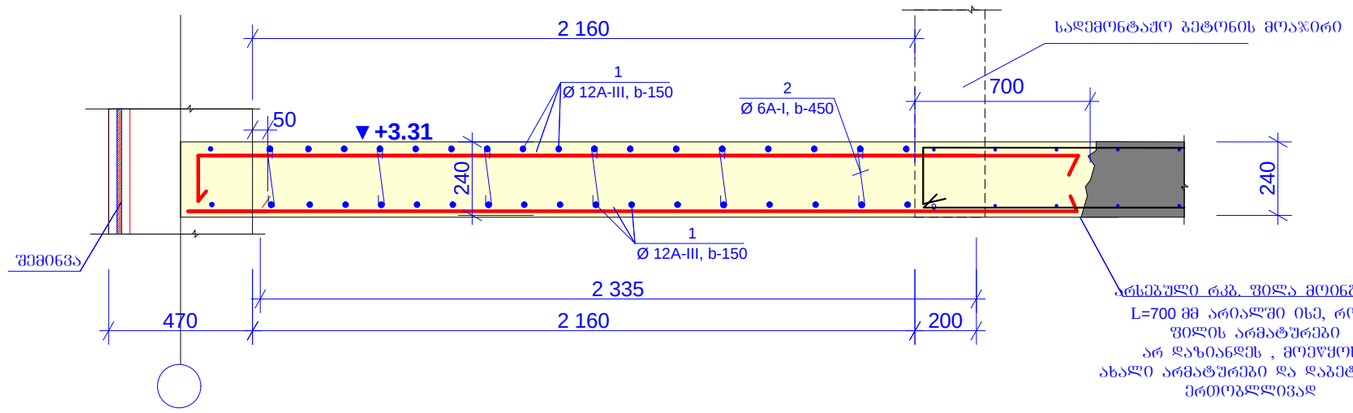

ფორ. A-3 | დაკვეთა

ექსპლიკაცია

პიროგითი ნიშნები

შენიშვნები:

დამკვეთი	ს.ს. თიბისი ბანკი
მისამართი	მარჯანიშვილის გამზირი №7
პროექტის სახელწოდება	ს.ს. თიბისი ბანკის ახალი სერვის ცენტრი ქ. თბილისი, აბაშიძის და არაქიშვილის კუთხე

თანამდებობა	გვარი	ხელმოწერა
დირექტორი	ზ. სუჯაშვილი	
არქიტექტორი	ბ. სუჯაშვილი	
კონსტრუქტორი	ლ.კვირიკაშვილი	

შ.პ.ს. „სუჯა“

კონსტრუქციული ნაწილი

მასშტაბი	1 : 100	კვეთი 1 - 1 კვეთი 2 - 2 კვეთი 3 - 3
თარიღი	2017 წ.	

სტადია	ფურცელი	ფურცლები
კ	კ-04	4